

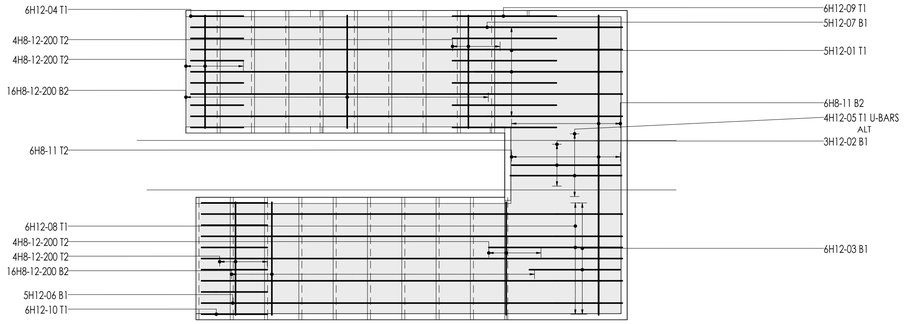


ST1 Plan
(Scale: 1 : 25)

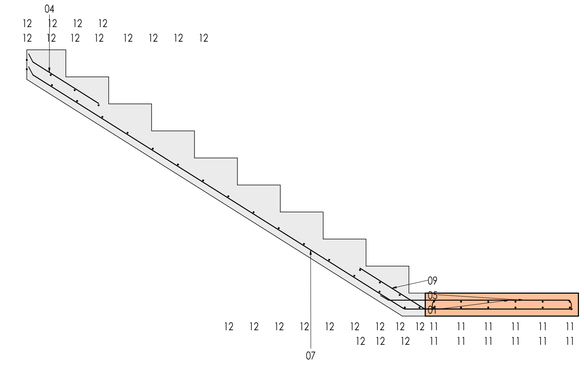


ST1 Flight 2 section
(Scale: 1 : 20)

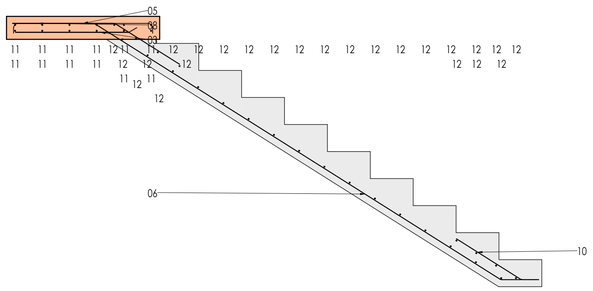

TYPICAL DETAIL ST1 - STAIR WITH LANDINGS

After SMDSC 4th ed. MD ST1 - confirm with design

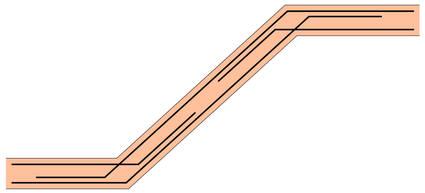


Main bars continuous round the outside corners of the knees; at the inside corners the bars cross, each run on straight to the far face and anchored there; top bars at the knees reach the greatest of 0.1 x span, a tension anchorage or 500; distribution bars as MD S1


TD ST1 - STAIR WITH LANDINGS

ST1 Flight 1 section
(Scale: 1 : 20)

SLAB / BASE (SECTION)

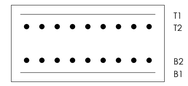

WALL (PLAN SECTION)
Near face

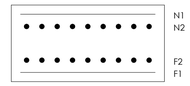

Far face

1 = outer layer, 2 = second layer

RC layer notation

REINFORCEMENT NOTES

1. Read with the general arrangement drawings and the general notes (0900). Do not scale from this drawing.
2. Concrete: stairs C40/50.
3. Reinforcement: high yield ribbed bars B500B to BS 4449, scheduled to BS 8666:2020. Bar schedules: 4523-01.
4. Nominal cover c_nom to all reinforcement, links included (includes delta c_dev = 10); to the general notes.
5. Maximum aggregate size 20 mm.
6. Bar notation: number, type and size, mark, centres, layer, e.g. 20H16-63-150 B1; centres and layer not given for beams and columns. Link zones (13@100): 13 links at 100 centres.
7. Layers: T top, B bottom, N near face, F far face; 1 outer layer, 2 second layer (see the layer notation key). EF each face, EW each way, ES each side, STG staggered, ALT alternate, ABR alternate bar reversed, UB U-bars (SMDSC 4th ed. Appendix I).
8. Laps and anchorages to the table in the general notes (0900) unless dimensioned; laps of adjacent bars staggered unless shown otherwise.
9. Bars bent cold to BS 8666; none heated, welded or rebent on site without approval.
10. Construction joints, holes and cast-in items only as shown or agreed.
11. Reinforcement inspected before concreting; no bar substituted without approval.
12. Fixing: Stairs: bars carried on spacers at 1.0 m centres max; landing bars lapped as dimensioned.
13. Typical details: TD ST1 (MD ST1) on drawing 4523 (after the SMDSC 4th ed. model details; confirm with design).

Rev.	Date	Description	Drawn by	Check by

NOSA Ltd.
Suite 9.1, 9th Floor, ICC
2A Main Street
Gibraltar, GX11 1AA
T: +350 20075000
M: +350 58008085 / +35057056000
e: info@nosa.gi

Client: Client X

Project Title: 1st Rock Street

Drawing Description: Stairs reinforcement

Drawing status: Project Status

Scale:	Size:	Date:	Drawn by:	Revision:
As shown	ISO A1	26/10/26	Author	

Drawing Number:

Project Number		Originator		Functional Breakdown		Spatial Breakdown		Form identifier		Discipline		Number
12345	-	NOSA	-	ZZ	-	ZZZ	-	D	-	S	-	4523