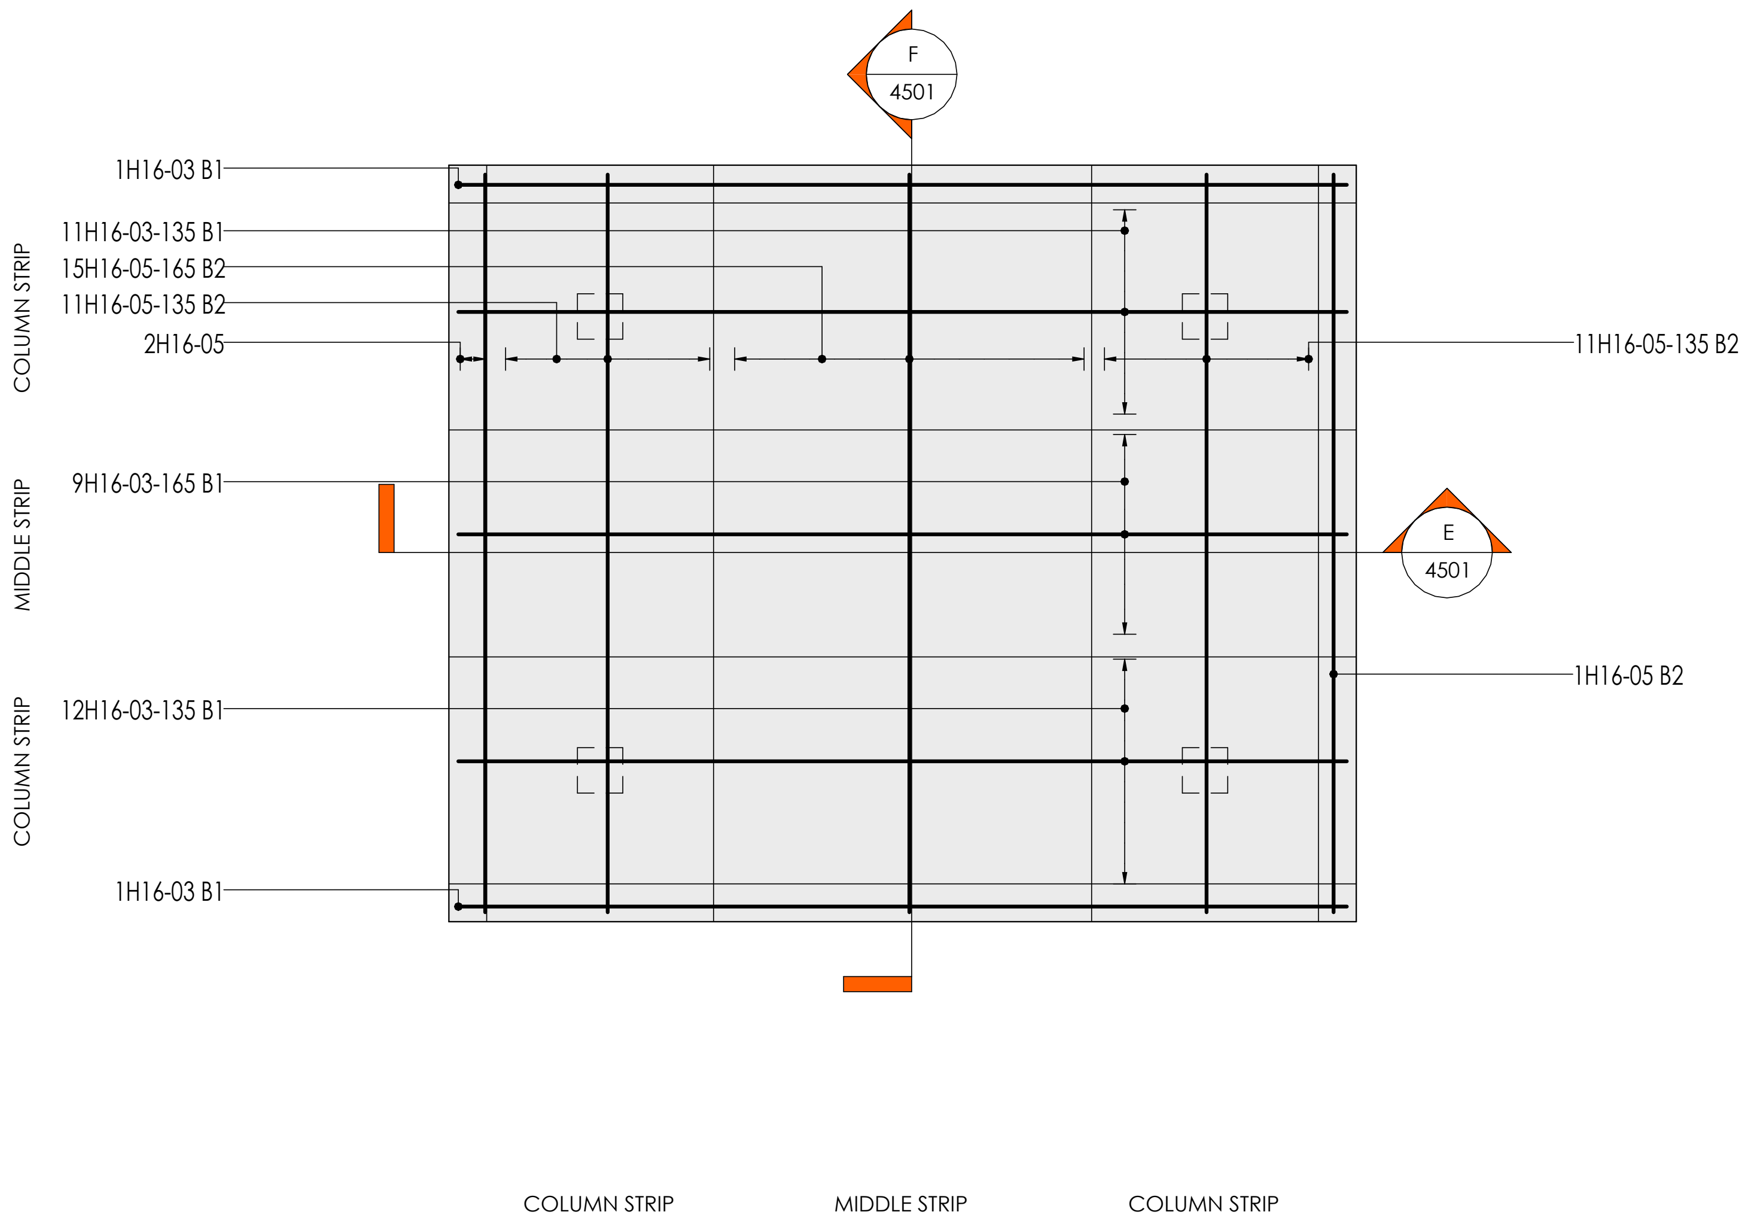
F
4501
1H16-03 B1
11H16-03-135 B1
15H16-05-165 B2
11H16-05-135 B2
2H16-05
11H16-05-135 B2
9H16-03-165 B1
E
4501
1H16-05 B2
12H16-03-135 B1
1H16-03 B1
COLUMN STRIP
MIDDLE STRIP
COLUMN STRIP
COLUMN STRIP
MIDDLE STRIP
COLUMN STRIP

## S20 Bottom reinforcement

(Scale: 1 : 50)

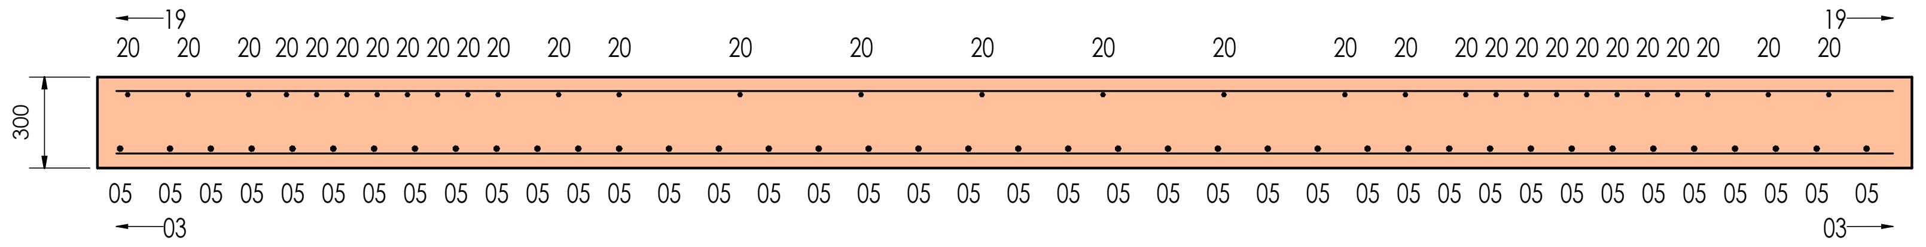
19
19
20 20 20 20 20 20 20 20 20 20 20 20 20 20 20 20 20 20 20 20 20 20 20 20 20 20 20 20 20 20 20
300
05 05 
03
03

## S20 Section E-E

(Scale: 1 : 25)

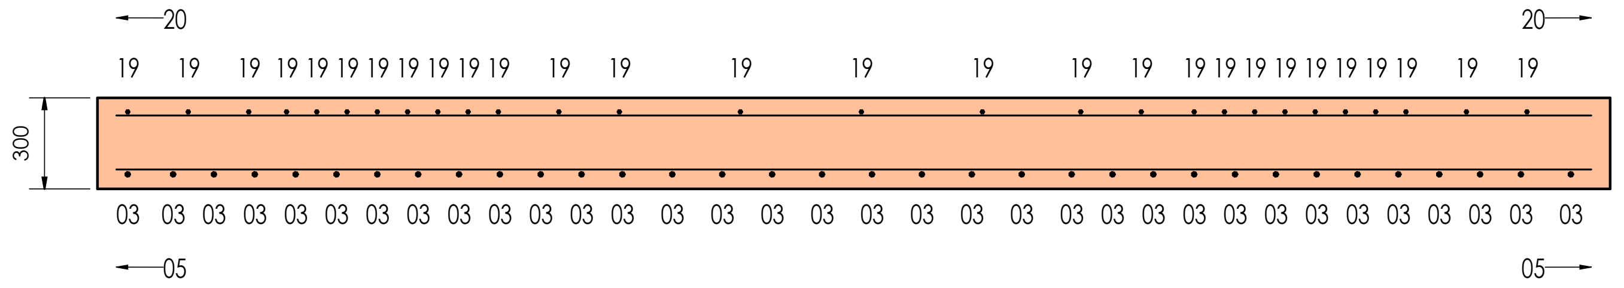
20
20
19 19 19 19 19 19 19 19 19 19 19 19 19 19 19 19 19 19 19 19 19 19 19 19 19 19 19 19
300
03 03 03 03 03 03 03 03 03 03 03 03 03 03 03 03 03 03 03 03 03 03 03 03 03 03 03 03 03 03 03 03 03 03
05
05

## S20 Section F-F

(Scale: 1 : 25)

TYPICAL DETAIL OP1 - SLAB OPENING TRIMMING

After SMDSC 4th ed. MD OP1 / 6.2.2.12 - confirm with design

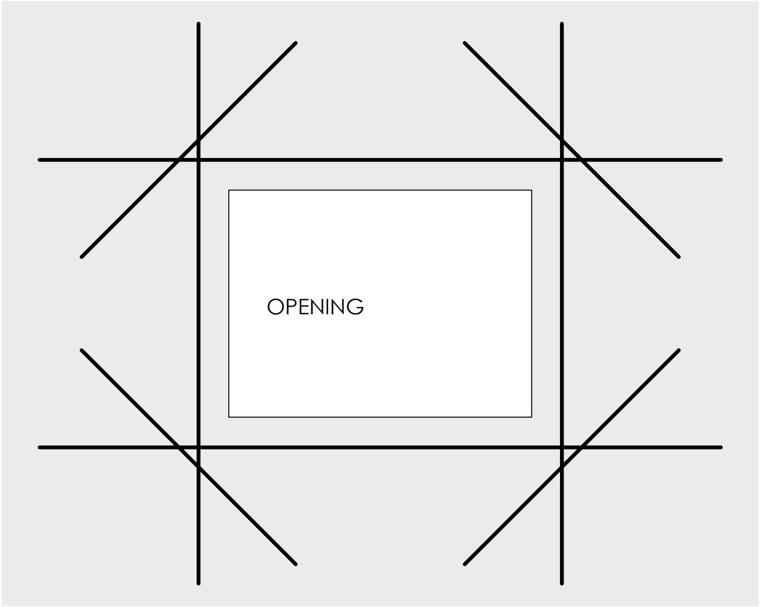

Trimmers of the area cut, half each side,
l_bd (450 min.) past the opening, clear of the mat
Openings 500-1000 in slabs over 250: corner
diagonals top and bottom, outside the opening

## TD OP1 - SLAB OPENING TRIMMING

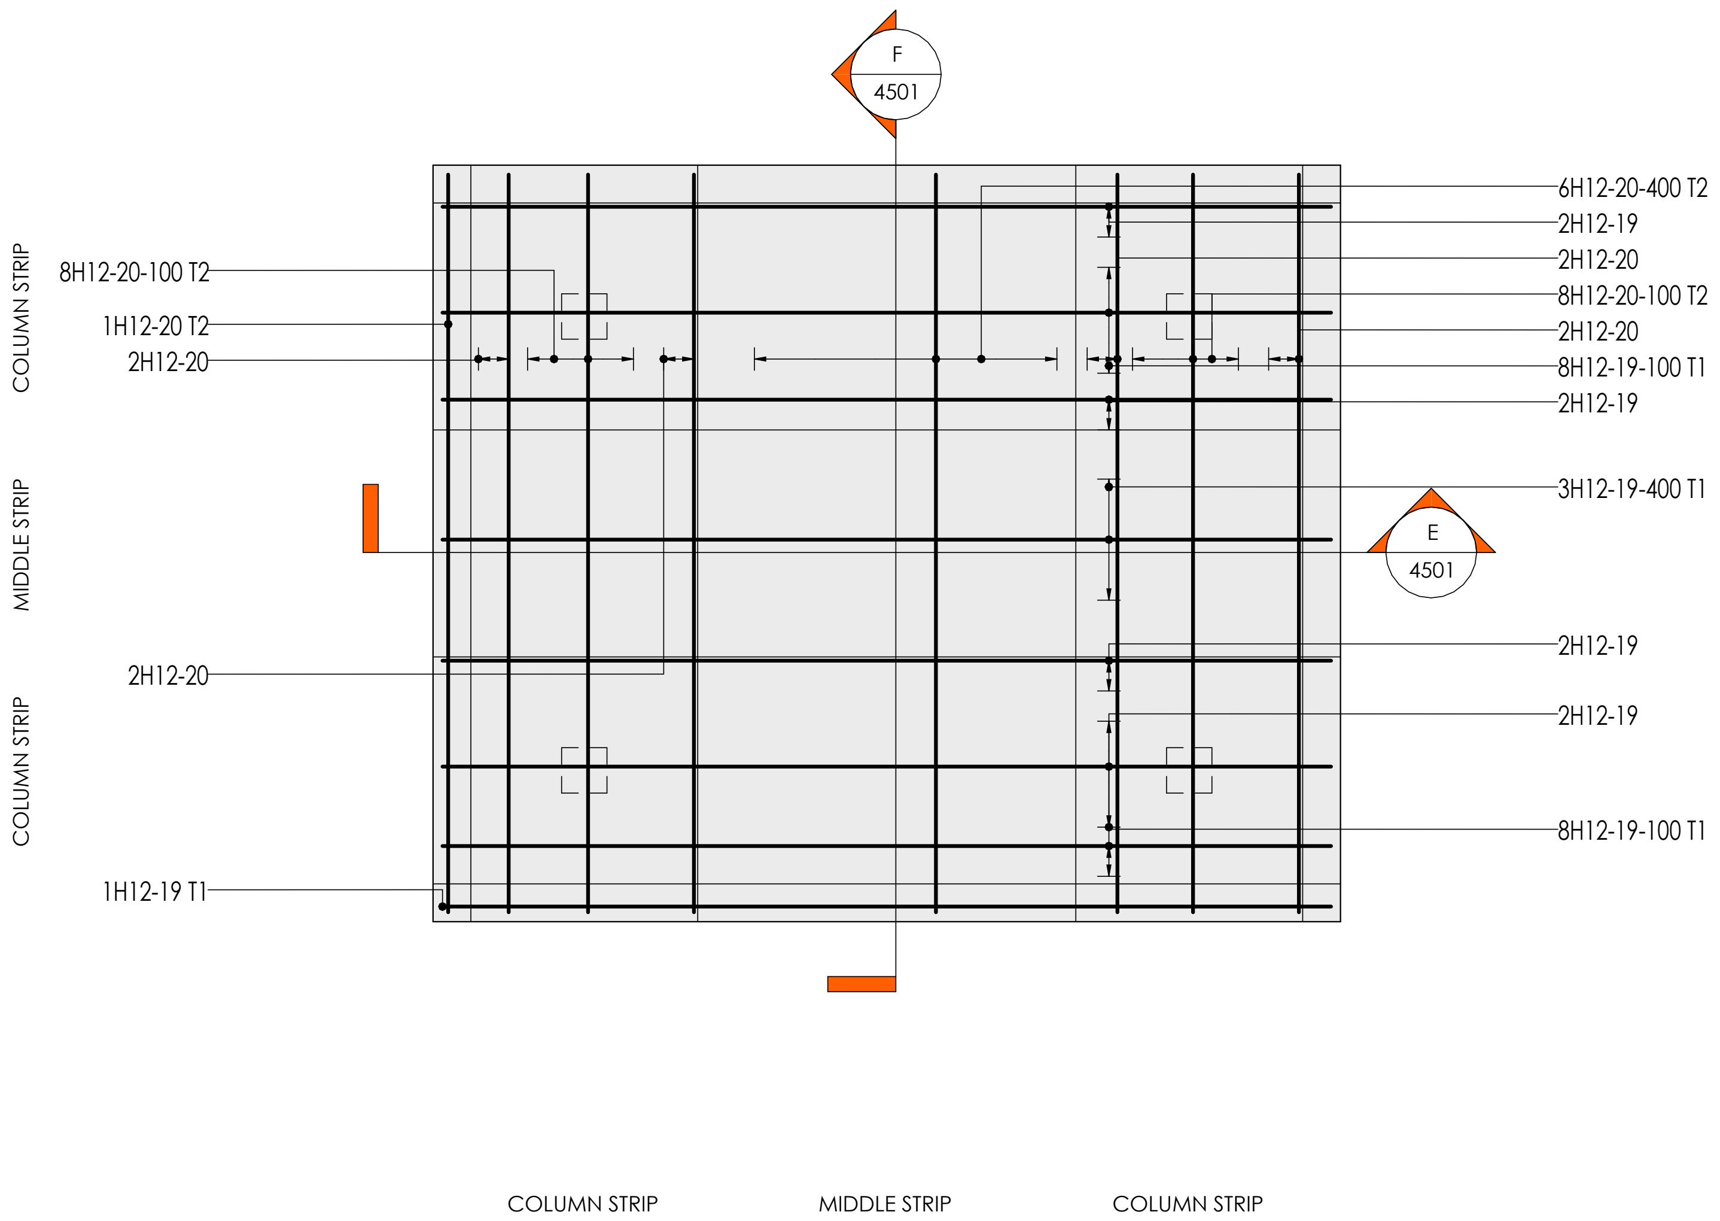
F
4501
8H12-20-100 T2
1H12-20 T2
2H12-20
2H12-20
1H12-19 T1
6H12-20-400 T2
2H12-19
2H12-20
8H12-20-100 T2
2H12-20
8H12-19-100 T1
2H12-19
3H12-19-400 T1
E
4501
2H12-19
2H12-19
8H12-19-100 T1
COLUMN STRIP
MIDDLE STRIP
COLUMN STRIP
COLUMN STRIP
MIDDLE STRIP
COLUMN STRIP

## S20 Top reinforcement

(Scale: 1 : 50)

TYPICAL DETAIL S1 - SLAB TOP BARS AT AN INTERNAL SUPPORT

After SMDSC 4th ed. MD S1 - confirm with design

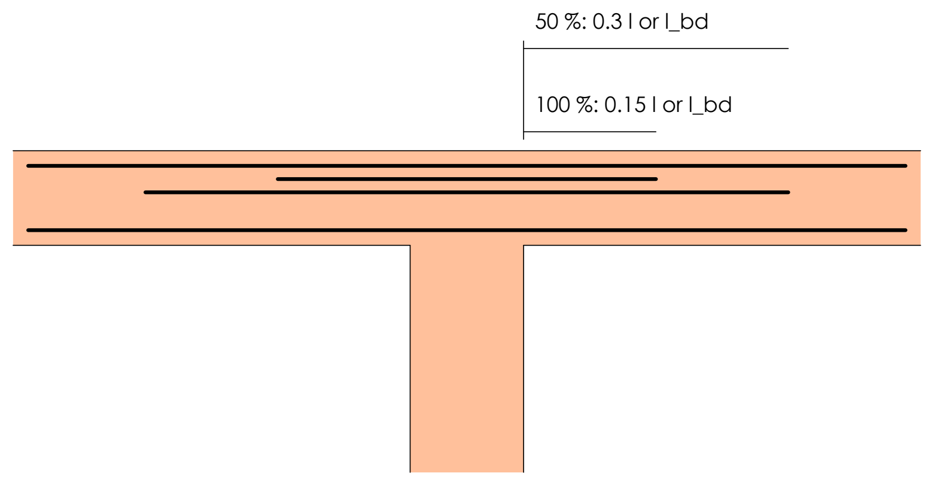
50 %: 0.3 l or l_bd
100 %: 0.15 l or l_bd

l = clear span, from the face of the support;
the greater of the two governs
Bottom bars: 40 % into the support, lapped
Distribution bars to the MD S1 table

## TD S1 - SLAB TOP BARS AT AN INTERNAL SUPPORT

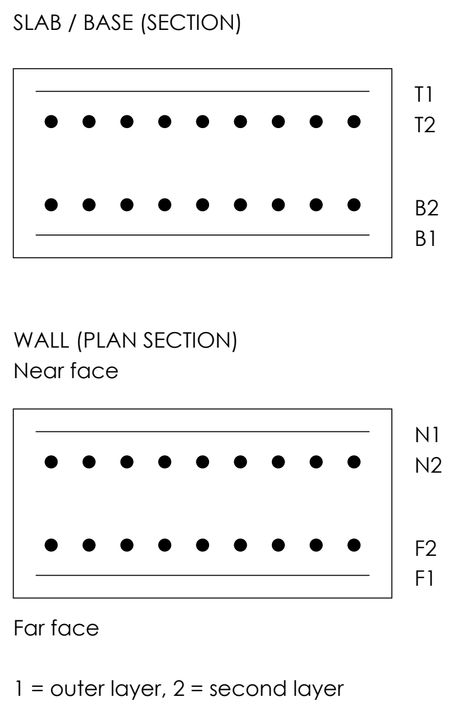
SLAB / BASE (SECTION)
T1
T2
B2
B1
WALL (PLAN SECTION)
Near face
N1
N2
F2
F1
Far face

1 = outer layer, 2 = second layer

## RC layer notation

REINFORCEMENT NOTES

1. Read with the general arrangement drawings 1000 series and the general notes (0900). Do not scale from this drawing.
2. Concrete: slabs C32/40.
3. Reinforcement: high yield ribbed bars B500B to BS 4449, scheduled to BS 8666:2020. Bar schedules: 4501-01.
4. Nominal cover c_nom to all reinforcement, links included (includes delta c_dev = 10): slabs 40.
5. Maximum aggregate size 20 mm.
6. Bar notation: number, type and size, mark, centres, layer, e.g. 20H16-63-150 B1; centres and layer not given for beams and columns. Link zones (13@100): 13 links at 100 centres.
7. Layers: T top, B bottom, N near face, F far face; 1 outer layer, 2 second layer (see the layer notation key). EF each face, EW each way, ES each side, STG staggered, ALT alternate, ABR alternate bar reversed, UB U-bars (SMDSC 4th ed. Appendix I).
8. Laps and anchorages to the table in the general notes (0900) unless dimensioned; laps of adjacent bars staggered unless shown otherwise.
9. Bars bent cold to BS 8666; none heated, welded or rebent on site without approval.
10. Construction joints, holes and cast-in items only as shown or agreed.
11. Reinforcement inspected before concreting; no bar substituted without approval.
12. Fixing: Slabs: bottom mat on spacers, top mat on chairs to BS 7973 chosen by the contractor (SMDSC 4th ed. 4.2.6); bars tied at alternate intersections, at every one along edges and round openings.
13. Buildability check: A+ (100/100; 0 error(s), 0 warning(s)) - see the RC QA report.
14. Typical details: TD S1 (MD S1), TD OP1 (MD OP1 / 6.2.2.12) on drawing 4501 (after the SMDSC 4th ed. model details; confirm with design).

| Rev. | Date | Description | Drawn by | Check by |
|---|---|---|---|---|

**NOSA Ltd.**
Suite 9.1, 9th Floor, ICC
2A Main Street
Gibraltar, GX11 1AA
T: +350 20075000
M: +350 58008085 / +35057056000
e: info@nosa.gi

Client: Client X

Project Title: 1st Rock Street

Drawing Description: Slabs reinforcement - S20

Drawing status: Project Status

| Scale: | Size: | Date: | Drawn by: | Revision: |
|---|---|---|---|---|
| As shown | ISO A1 | 10/18/26 | Author | |

Drawing Number:

| Project Number | | Originator | | Functional Breakdown | | Spatial Breakdown | | Form identifier | | Discipline | | Number |
|---|---|---|---|---|---|---|---|---|---|---|---|---|
| 12345 | - | NOSA | - | | - | | - | | - | | - | 4501 |